

A liberação ou aprovação não exime o projetista de responsabilidade sobre o documento.
Este documento é propriedade da VPM TRECHO 3 e seu conteúdo não pode ser revelado a terceiros sem autorização expressa.

Classificação: DE-O-R1-076-100-9999-6-A99-201
Nº Controle: BR8368-5

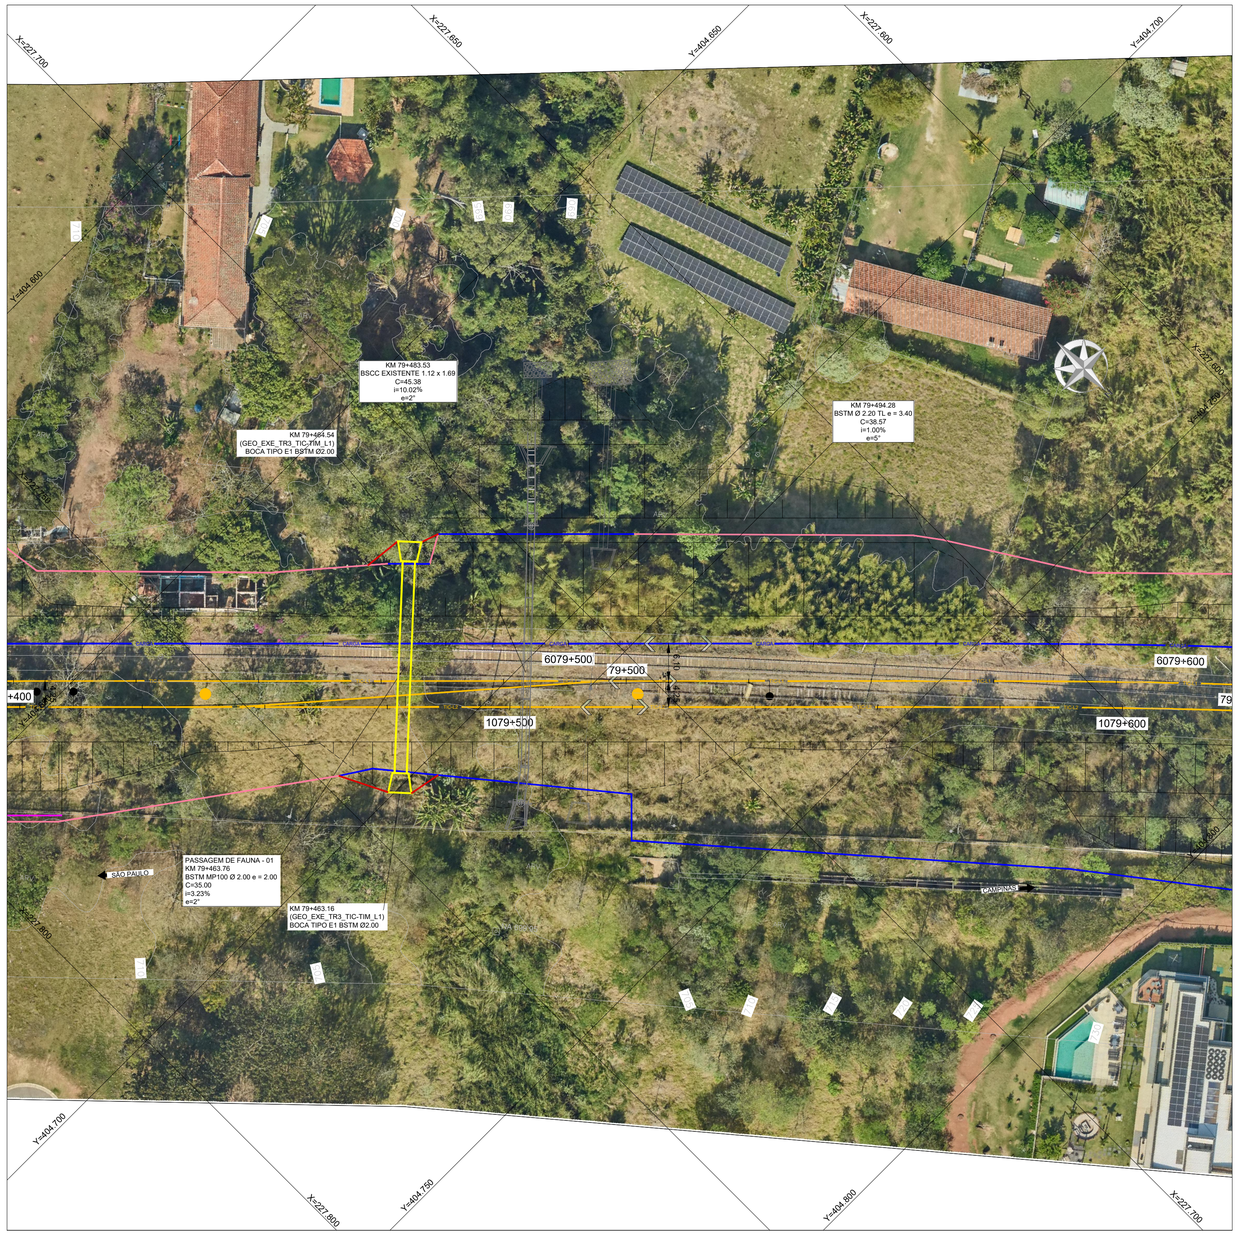


PLANTA
ESCALA 1:500

SEÇÃO TRANSVERSAL - METÁLICA
ESC.1:50

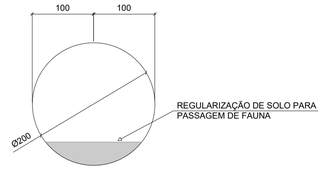

NOTA: A PASSAGEM DE FAUNA APRESENTADA TRABALHA DE FORMA SECA.

PERFIL - PASSAGEM DE FAUNA - T3B_PF_01

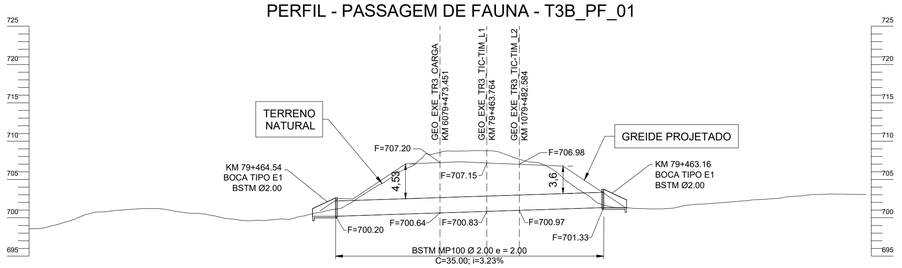

CORTE LONGITUDINAL
ESCALA 1:400

LEGENDA OBRAS COMPLEMENTARES

- MURO DE VEDAÇÃO PRÉ-MOLDADO PROJETADO
- MURO DE VEDAÇÃO MOLDADO IN LOCO PROJETADO
- ALAMBRADO
- CERCA - DIRECIONAMENTO DE FAUNA
- CONTENÇÃO ATERRO
- CONTENÇÃO CORTE
- LINHA TIC-L1
- LINHA TIC-L2
- LINHA TIC-EST.
- LINHA CARGA
- FAIXA DE DOMÍNIO EXISTENTE
- FAIXA DE DOMÍNIO PROJETADA
- BORDO
- TALUDE DE ATERRO
- TALUDE DE CORTE
- PASSAGEM DE FAUNA

NORTE

LEGENDA TOPOGRAFIA E CADASTRO

- CURVA DE NÍVEL MESTRA
- CURVA DE NÍVEL INTERMEDIÁRIA
- MARCO QUILOMETRAGEM
- POSTE DE REDE AÉREA
- POSTE DE ENERGIA
- POSTE DE ILUMINAÇÃO
- POSTE COM TRANSFOMADOR
- POSTE DESATIVADO
- PLACA DE SINALIZAÇÃO
- VERT. PRINCIPAL/SUPERIOR/APOIO
- BOCA DE LOBO / BOCA LEÃO
- AÇUDE, LAGO E INTERMITENTE
- BASE DE ANCORAGEM
- BANGALÔ
- TORRE CPTM
- BOMBA DE IMPEDÂNCIA
- OAE EXISTENTE
- CERCA EXISTENTE
- MURO EXISTENTE
- GRADIL E ALAMBRADO
- MÁQUINA DE CHAVE
- SEMÁFORO
- SINAL ALTO / SINAL ANÃO
- RADAR
- ARMÁRIO
- CAIXA
- INÍCIO AGULHA/COICE
- ARV.ISOLADA/ MASSA ARB.
- PONTO DE ÔNIBUS
- PARA CHOQUE VIA
- PÓRTICO , BASE E LONGARINA
- FAIXA DE DOMÍNIO EXISTENTE
- EDIFICAÇÃO

REFERÊNCIA:

- DE-O-R1-076-100-9999-6-C01-000 [LEVANTAMENTO TOPOGRÁFICO]
- DE-V-R1-076-100-0199-6-U01-100 [PROJETO DE GEOMETRIA]
- DE-O-R1-076-100-9999-6-A99-000 [PROJETO DE OBRAS COMPLEMENTARES]

NOTAS:

1. MEDIDAS EM METROS, EXCETO ONDE INDICADO;
2. SISTEMA DE COORDENADAS TOPOGRÁFICAS LOCAL: STL-NOROESTE;
3. ESPESSURA DA CHAPA FOI ADOTADA DE ACORDO COM O CATÁLOGO TÉCNICO VIGENTE DA ARMCO PARA BUEIROS METÁLICOS.

REV.	ÁREA	RESP.	APROV.	DATA
				/ /
				/ /
				/ /
				/ /
				/ /
				/ /
				/ /
				/ /
1B	OBC	LFS	-	13/03/2026
1A	OBC	LFS	-	19/01/2025

SUPERVISORA

PROJETISTA: egis ENGENHARIA E CONSULTORIA LTDA.

TIC TRENS

Nº CONTRATO	001/2024
RESPONSÁVEL TÉCNICO/DATA	LUIZ F SIVIERO CREA 5061705205 ART 2620250260177 01/04/2025
APROVAÇÃO/DATA	
ÁREA	
RESPONSÁVEL TÉCNICO/DATA	
APROVAÇÃO/DATA	

PROJETO: TIC EIXO NORTE - CIVIL
PROJETO EXECUTIVO - PASSAGEM DE FAUNA
PROJETO DE OBRAS COMPLEMENTARES

TÍTULO: VPM TRECHO 3 - JUNDIAÍ – CAMPINAS
LOUVEIRA – VINHEDO – 3B
OBRAS COMPLEMENTARES -
DETALHES PASSAGEM DE FAUNA

CLASSIFICAÇÃO

TIPO	SIST.	LINHA	TREC.	SUB TR.	SUB SIST.	ETAP.	CLASSE	SEQUE.	Nº DE CONTROLE
DE - O - R1 - 076 - 100 - 9999 / 6 - A99 - 201									BR8368-5

VER ÍNDICE DE DOCUMENTOS	ESCALA	REVISÃO	FOLHA
BN0219-9	INDICADA	01	001/001